
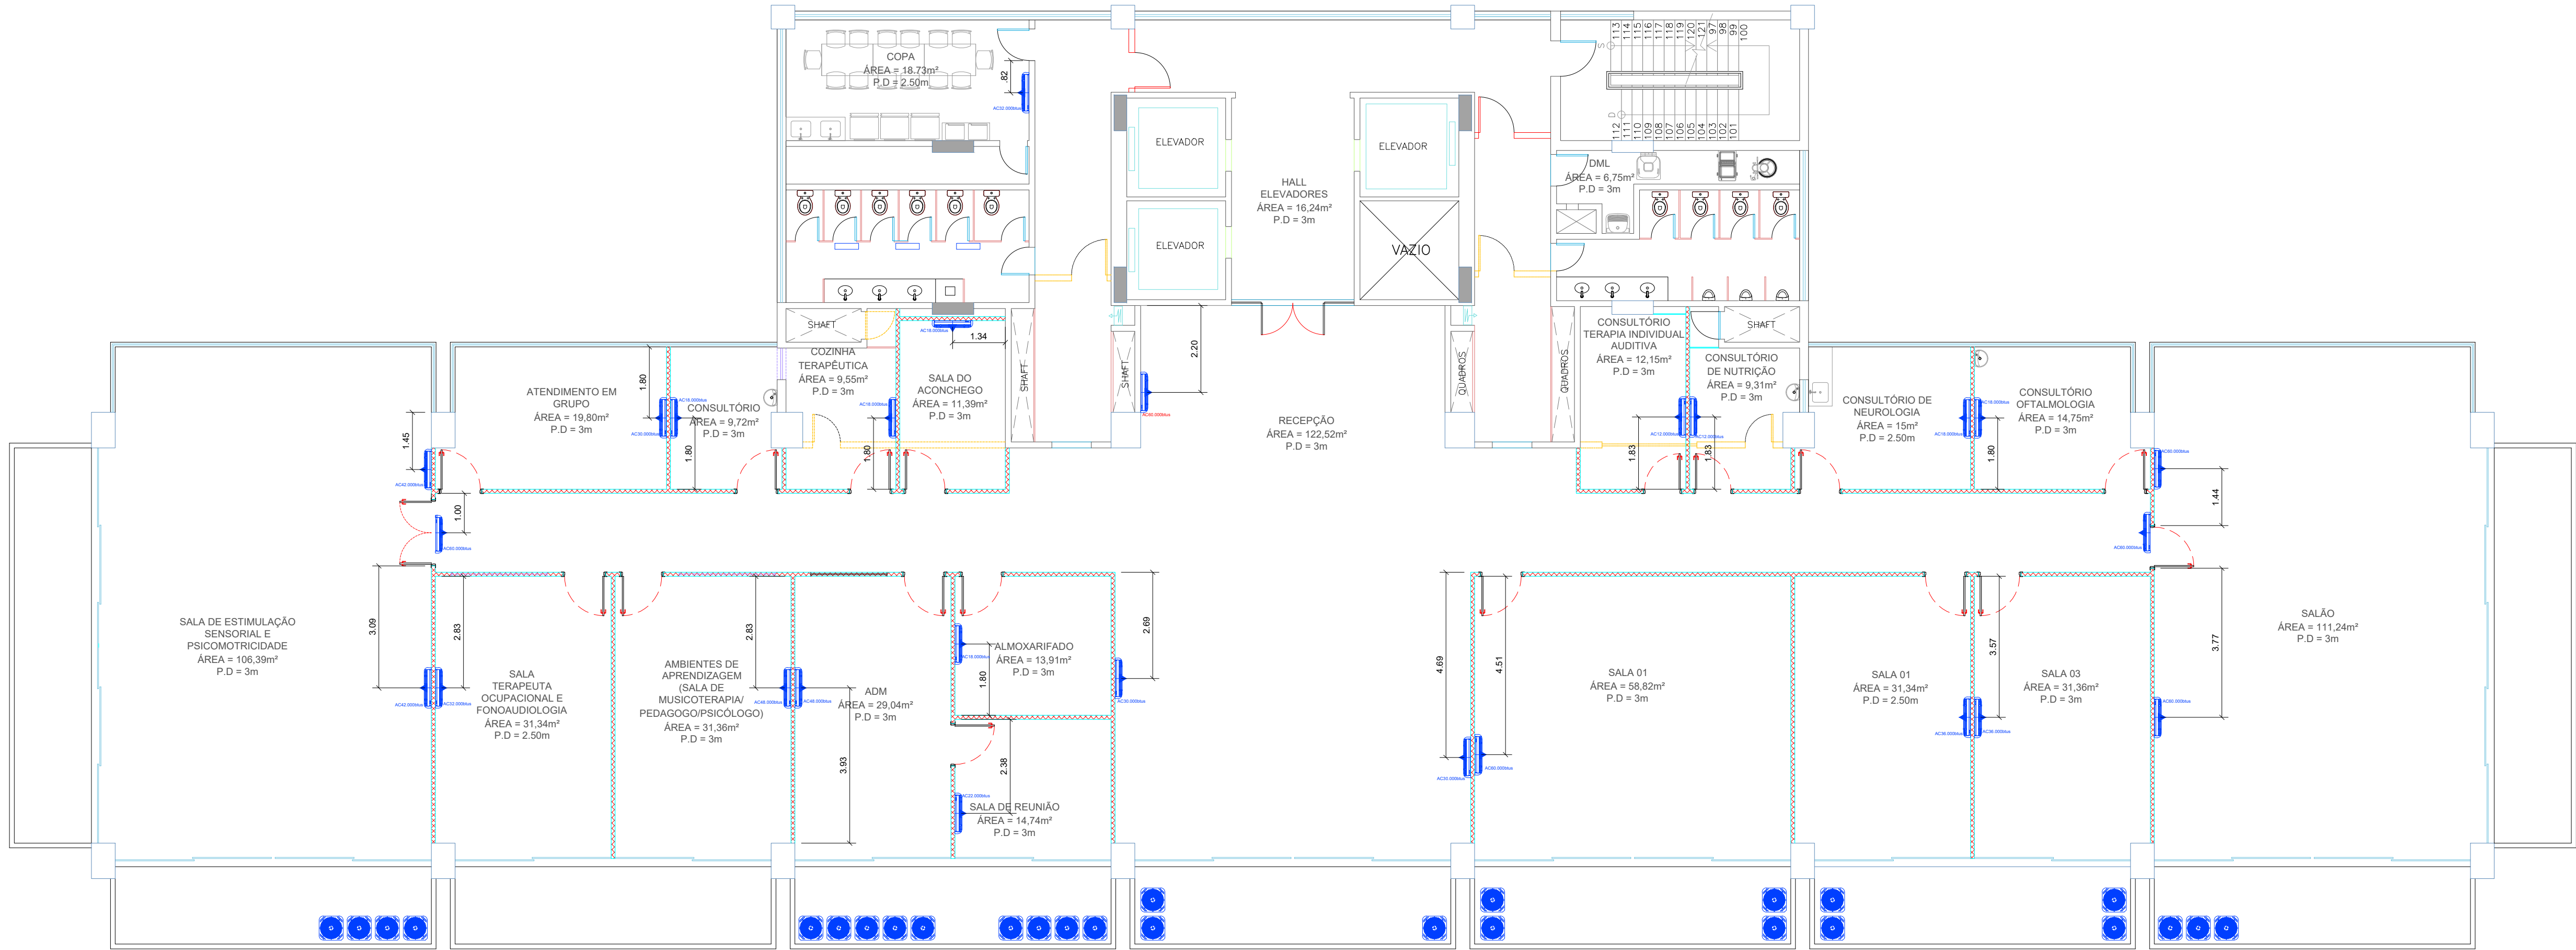


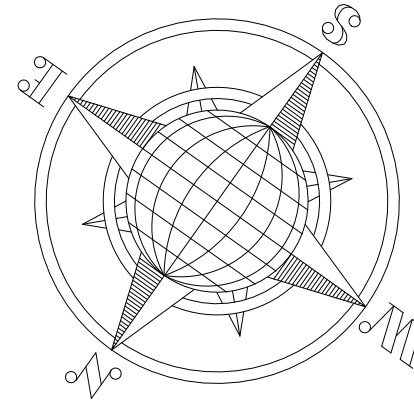

01 PLANTA BAIXA - SETORIZAÇÃO CEDTEA E CER III
ESCALA 1/100

LEGENDA DE ELÉTRICA E REDE	
	PONTO DE TOMADA UNIVERSAL ESTABILIZADA
	PONTO DE TOMADA UNIVERSAL BAIXA (h=0.30m)
	PONTO DE TOMADA UNIVERSAL MÉDIA (h=1.30m)
	PONTO DE TOMADA UNIVERSAL ALTA (h=2.30m)
	PONTO PARA REDE DE LÓGICA BAIXO (h=0.30)
	PONTO DE TELEFONE (h=0.30m)
	INTERRUPTOR PARA UMA SEÇÃO
	INTERRUPTOR PARA DUAS SEÇÕES
	INTERRUPTOR PARALELO OU THREE-WAY
	PONTO DE ANTENA (h=2.30m)
	DUCHA HIGIÊNICA (h=0.30m)
	ACCESS POINT (h=2.30m)
	RACK COM VENTILAÇÃO FORÇADA PARA SWITCH 24 PORTAS
	PONTO DE ÁGUA P/ FILTRO (h=1.30m)
	RELÓGIO DE REGISTRO DE PONTO
	CAMERA DE CFTV
	QUADRO DE LUZ (h=1.30m)
	LUMINÁRIA DE SOBREPOR 2X9/10W LED - DIFUSOR LEITOSO. MEDIDAS: 55X140X630mm
	LUMINÁRIA DE SOBREPOR P/ PAREDE (ARANDELA) EM ALUMÍNIO INJETADO C/PINTURA ELETROSTÁTICA POLIÉSTER NA COR BRANCA
	AR CONDICIONADO TIPO SPLIT - UNIDADE CONDENSADORA
	AR CONDICIONADO TIPO SPLIT - UNIDADE EVAPORADORA
	EXAUSTOR DE PAREDE(CIRCUITO EXCLUSIVO)
	RALO
	NOVO PADRÃO DE ENTRADA DE ENERGIA
	BEBEDOURO ELÉTRICO EM AÇO INOXIDÁVEL (MOD. DE PÉ ADULTO/CRANÇA)
	NOBREAK
	SPLITVENT RENOVADOR/INSULADOR DE AR BIVOLT
	BLOCO AUTÔNOMO - LUZ DE EMERGÊNCIA LUMINÁRIA LAMPADA 30 LED DURAÇÃO DE ATÉ 6H COR BRANCO

LEGENDA:	
	ELEMENTO A DEMOLIR
	ELEMENTO A CONSTRUIR
	DIVISÓRIAS EM PLACAS DE GESSO ACARTONADO
	PROJEÇÃO SUPERIOR

NOTAS

- 01 - MEDIDAS DE COTAS ACABADAS.
- 02 - TODAS AS MEDIDAS DO PROJETO DEVEM SER AFERIDAS IN LOCO PARA A EXECUÇÃO DA OBRA.
- 03 - ESTA PLANTA APRESENTA UM CROQUI PARA UMA ADEQUAÇÃO SIMPLES. É ESSENCIAL AVALIAR A NECESSIDADE DE INSTALAÇÕES ELÉTRICAS, HIDRÁULICAS, DE AR-CONDICIONADO, BEM COMO DETALHES CONSTRUTIVOS E DE MARCENARIA. PARA ESSES ASPECTOS, RECOMENDA-SE A CONSULTA AO NÚCLEO DE ENGENHARIA.
- 04 - TODAS AS TUBULAÇÕES E ELETRODUTOS DEVERÃO SER EMBUTIDOS.
- 05 - NENHUMA INSTALAÇÃO NOVA DEVERÁ SER APARENTE.
- 06 - DEVERÁ SER INSTALADO NAS ÁREAS DESTINADAS AOS AMBIENTES DO CEDTEA, ISOLAMENTO ACÚSTICO DENTRO DAS ESTRUTURAS DE DRYWALL COM LÁ DE ROCHA OU DE VIDRO.
- 07 - PORTAS DOS AMBIENTES DESTINADOS AO ATENDIMENTO DO CEDTEA, DEVEM POSSUIR TRATAMENTO ACÚSTICO.
- 08 - TODAS AS ESPECIFICAÇÕES DE ACABAMENTOS E MOBILIÁRIOS DEVEM SEGUIR AS DIRETRIZES ESTABELECIDAS NO CADERNO TÉCNICO CEA.

* QUALQUER DÚVIDA, ENTRAR EM CONTATO COM O NÚCLEO DE ENGENHARIA.

24/02/2026	04	Felipe	01	ADICÃO DO CERIII
06/02/2026	03	Felipe	01	ALTERAÇÃO DE LAYOUT CONFORME SOLICITAÇÃO DA CEA
29/01/2026	02	Felipe	01	ALTERAÇÃO DE AMBIENTES POR SOLICITAÇÃO DA CAP 3.3
21/01/2026	01	Felipe	01	EMIÇÃO INICIAL
Data	Revisão	Revisor	Folha	Descrição
ASSOCIAÇÃO PAULISTA PARA O DESENVOLVIMENTO DA MEDICINA Associação de Profissionais da Medicina e da Saúde Programa de Atenção Integral à Saúde				
Aprovação (Data/Assinatura)				
Unidade				
AP 3.3 - CEDTEA				
Local	Pavimento			Folha
R HANNIBAL PORTO, Nº 450, 4º PV - IRAJÁ, RIO DE JANEIRO - RJ, 21230-330	4º			01
Assunto	Data			01
PROJ. AR CONDICIONADO - CEDTEA E CERIII	25/02/2026			
Projeto	Responsável Legal			Planta de
FELIPE LARANJEIRA ABAL				ARQUIT.
Responsável Técnico - CREA:	Escala			
LUIGI GIGLIO	1/100			
	Diretoria de Projetos			
	ROSIANE N. DO NASCIMENTO			