


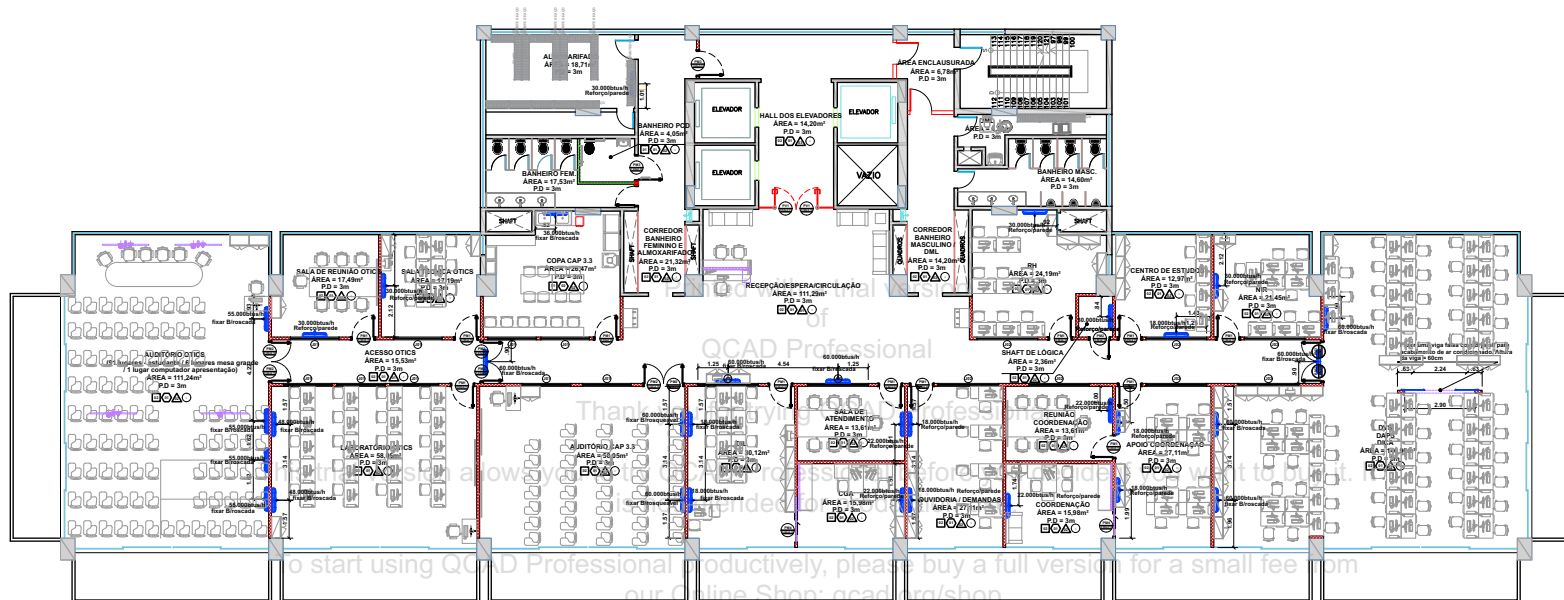

01 PLANTA BAIXA CAP 3.3 - 5 PV
ESCALA 1/100

QUADRO DE ESQUADRIAS			
COD.	DESCRIÇÃO	DIMENSÃO	PEITORIL
PM 01	PORTA DE DOBRADIÇA NA COR BRANCA	0,90m x 2,10m	-
PM 02	PORTA DE DOBRADIÇA NA COR BRANCA	0,90m x 2,10m	-
PM 03	PORTA DE DOBRADIÇA NA COR BRANCA	1,00m x 2,10m	-
PM 04	PORTA DE CORREIA INTERNA	0,90m x 2,10m	-
ESQUADRIAS DE ALUMÍNIO			
J01	JANELA FIXA - ALUMÍNIO BRANCO	2,00m x 1,00m	H = 1,10m
J02	JANELA FIXA - ALUMÍNIO BRANCO	2,00m x 1,00m	H = 1,10m
ESQUADRIAS DE VIDRO			
PV 01	PORTA DE VIDRO LAMINADO 10mm	0,90m x 2,10m	-

PARADE
1 - PINTURA EM PAREDES INTERNAS COM ACRILICA ACETINADA NA COR ALGODÃO EGÍPCIO SUVIVEL EQUIVALENTE TÉCNICO INCLUSIVE LIVAMENTO, 1 DEMÃO DE SELADOR ACRILICO, 2 DEMÃOS DE MASSA CORRIDA LIXADAS E 2 DEMÃOS DE ACABAMENTO.
2 - PINTURA EM PAREDES INTERNAS COM ACRILICA ACETINADA NA COR BRANCO NEVE CORAL, SUVIVEL EQUIVALENTE TÉCNICO INCLUSIVE LIVAMENTO, 1 DEMÃO DE SELADOR ACRILICO, 2 DEMÃOS DE MASSA CORRIDA LIXADAS E 2 DEMÃOS DE ACABAMENTO.
3 - PINTURA EM PAREDES INTERNAS COM ACABAMENTO "TUOLUOLHO" PINTAR COM A MESMA COR E TEXTURA EXISTENTE.
4 - REVESTIMENTO DE PAREDE RETIFICADO FORMA BRANCO AC - 32, 5X95CM, COR BRANCA DA ELIANE
PISO
1 - PISO CERÂMICO PANNA PLUS NA DIMENSÃO 60 X 60CM, COR BEGE, DA EXMNE EQUIVALENTE TÉCNICO.
OBS: CASO SE ESGOTEM TODAS AS POSSIBILIDADES DE ENCONTRAR A CERÂMICA PANNA PLUS NATUZZI FORÇA LAMINADO TÉCNICO RETIFICADO 60X60CM PLATO CONCRETO NATURAL DA ELIANE EQUIVALENTE TÉCNICO.
2 - ÁREA DE APLICAÇÃO DO PISO VINÍLICO.
RODAPE
1 - RODAPE DE POLIESTIRENO NA COR BRANCA - 10CM DE ALTURA
2 - RODAPE CERÂMICO SEGUNDO O PADRÃO DO PISO - 10CM DE ALTURA

LEGENDA:
----- ELEMENTO A DEMOLIR
----- ELEMENTO A CONSTRUIR
----- DIVISÓRIAS EM PLACAS DE GESSO ACARTONADO
----- DIVISÓRIAS EM PLACAS DE GESSO ACARTONADO VERDE (RESISTENTE À ÁGUA)
----- ALVENARIA EXISTENTE
----- ELEMENTO SUPERIOR
----- ELEMENTO INFERIOR

NOTAS
01 - MEDIDAS DE COTAS ACABADAS.
02 - TODAS AS MEDIDAS DO PROJETO DEVEM SER AFERIDAS IN LOCO PARA A EXECUÇÃO DA OBRA.
03 - ESTA PLANTA APRESENTA UM CROQUI PARA POSICIONAMENTO DE MAQUINÁRIO DE AR-CONDICIONADO
04 - TODAS AS TUBULAÇÕES E ELETRODUTOS DEVERÃO SER EMBUTIDOS.
05 - NENHUMA INSTALAÇÃO NOVA DEVERÁ SER APARENTE.
06 - TODAS AS ESPECIFICAÇÕES DE ACABAMENTOS MOBILIÁRIOS DEVERÃO SER DIRETRIZES ESTABELECIDAS NO CADENHO TÉCNICO CEA.
* QUALQUER DÚVIDA, ENTRAR EM CONTATO COM O NÚCLEO DE ENGENHARIA.

Histórico de Revisões			
Data	Revisão	Por	Descrição
28/05/2024	R05	Felipe	REVISÃO APÓS ALTERAÇÕES SOLICITADAS PELA CAP 3.3
28/05/2024	R04	Felipe	REVISÃO APÓS ALTERAÇÕES SOLICITADAS PELA CAP 3.3
28/05/2024	R03	Felipe	REVISÃO APÓS ALTERAÇÕES SOLICITADAS PELA CAP 3.3
21/05/2024	R02	Felipe	REVISÃO APÓS ALTERAÇÕES SOLICITADAS PELA CAP 3.3
11/05/2024	R01	Felipe	REVISÃO APÓS REUNIÃO COM A CAP 3.3
08/01/2024	R00	Felipe	EMISSION INICIAL
Aprovação (assinatura)			
Associação Fauista para o Desenvolvimento da Medicina			
Programa de Atenção Integral à Saúde			
Unidade			
AP 3.3 - CAP 3.3			
Local			
R HANNIBAL PORTO, Nº 450, 5º PV - IRAJÁ, RIO DE JANEIRO - RJ, 21230-330			
Projeto			
PROJ. ARQUITETURA - CAP 3.3 - POSICIONAMENTO DE EQUIPAMENTOS DE AR - CONDICIONADO			
FELIPE LARANJEIRA ABAL			
Responsável Técnico - CREA			
LUIGI GIGLIO			
Escala			
1/100			
Planta de			
ARQUIT.			
Diretor de Projetos			
ROSILANE N. DO NASCIMENTO			